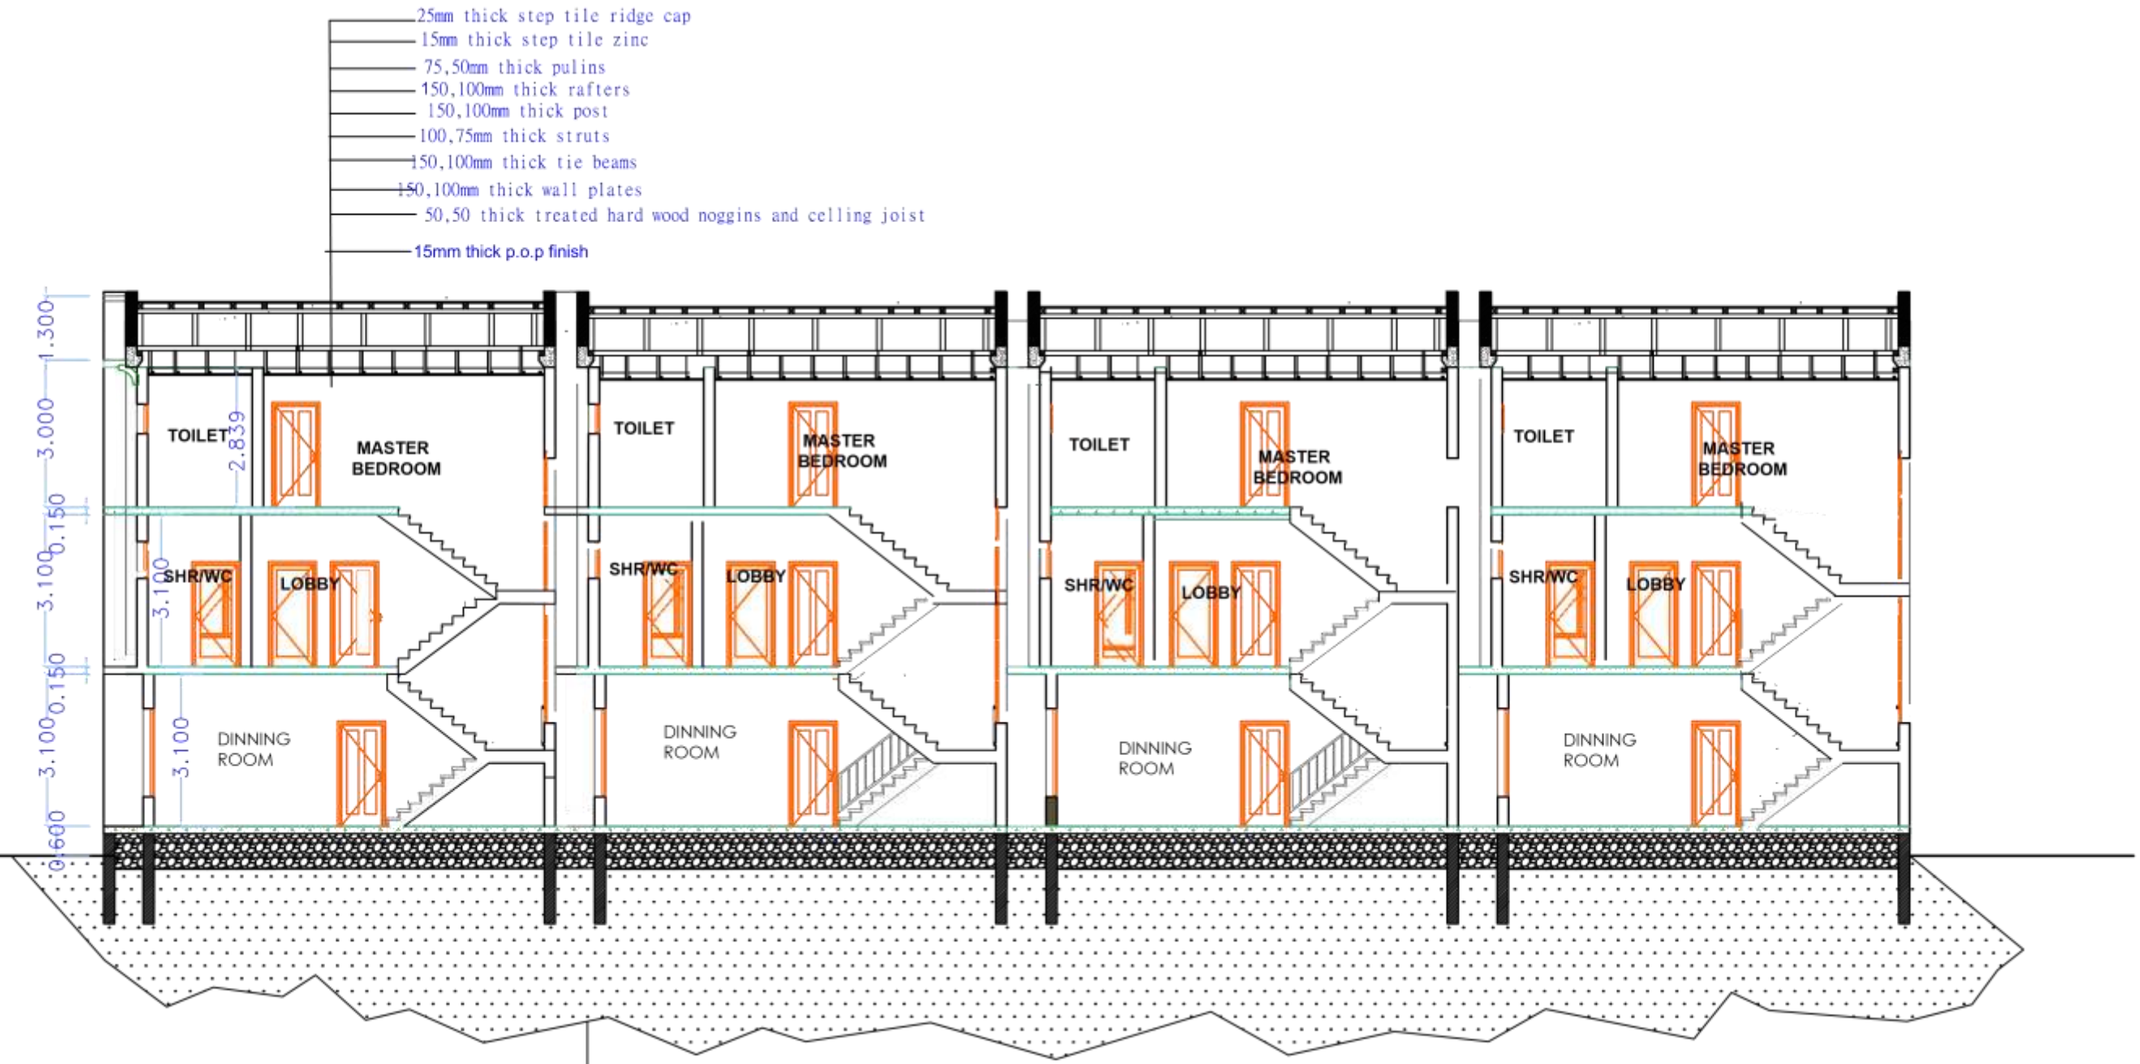

- 300*300 Glazed Vetrified Tile Floor Finish
- 150mm Plain Concrete Floor Plan Slab
- DPM
- 600mm Lump Stone Hardcore
- Laterite Earth Filling
- 230*230*460mm Block wall Filled with Weak Concrete
- 230*675mm Contineous Concrete Strip Foundation

Client nwigiri joshua	PROJECT: [PROJECT]	1. All dimensions are in millimeters (mm) 2. All figured dimensions are to be read as written and not scaled. 3. This drawing should be read in conjunction with all other drawings supplied for the execution of the works described in these drawings.	DRAWING TITLE: Location 25 badagry estate	DESIGN & DRAWN BY	CHRIS IHAZA	WORKING DRAWINGS
				CHECKED BY	ARC. ANTHONY C. N	
				SCALE:	1:125	SWD/06
				DATE:	08/08/2025	